


STILTED HOUSE / WANG HSIAO-KUEI ARCHITECTURE STUDIO

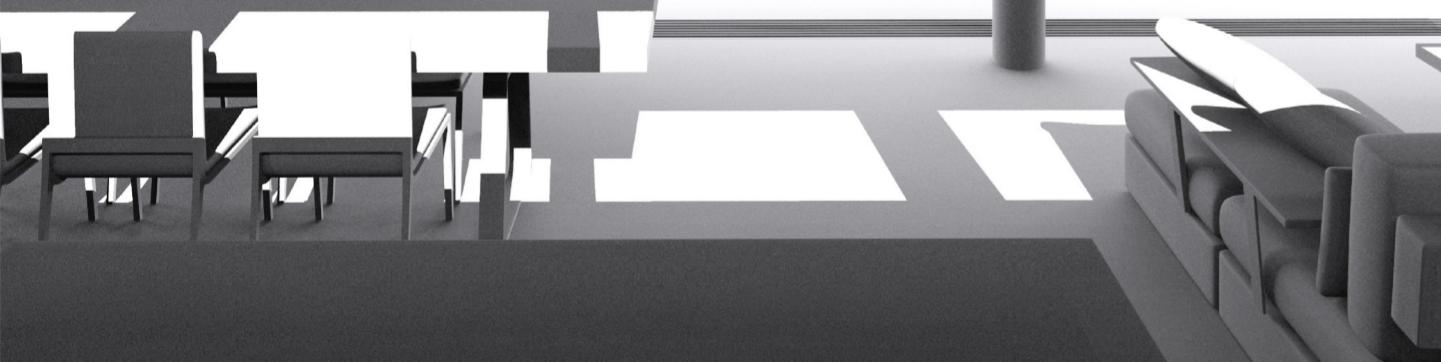

Studio:
Collocazione:
Architetto:
Collaboratori:
Area:
Anno:
Fotografo:

Wang Hsiao-Kuei Architecture Studio
Taiwan
Wang Hsiao-Kuei
Hong Zi-Ning
280.0 mq
2016
Cheng Chin-Ming


Stilted House è situata su una collina a Yunlin. Per ridurre l'impatto ambientale e preservare il paesaggio originale, la casa è sollevata su palafitte, offrendo così un'ampia vista sulla costa occidentale di Taiwan. La filosofia che avvolge l'intera casa a partire dalla forma deriva dalle credenze religiose del committente che sostiene una vita semplice e naturale dove l'ornamento diventa la qualità del materiale.

Lo spazio abitativo è coperto da un tetto a spiovente che crea un ambiente alto e spazioso, e la presenza di ampie vetrate ne permette l'illuminazione.


Il grande open space che costituisce la zona giorno è il fulcro dell'abitazione. Al suo interno si trovano la zona living, la zona pranzo e la cucina in stile Nakajima. Le pareti esposte a nord-ovest e nord-est sono costituite da pannelli vetrati con telaio in legno, che scorrono per l'intera lunghezza creando così un contatto diretto con il paesaggio esterno.

La zona notte è costituita da quattro suite comprendenti ciascuna un bagno privato. I mobili sono semplici ed essenziali e conferiscono un aspetto armonioso agli ambienti.


L'uso dell'acciaio consente la riduzione dell'uso del calcestruzzo e rende la costruzione più versatile sul versante della montagna, riducendo l'impatto ambientale.

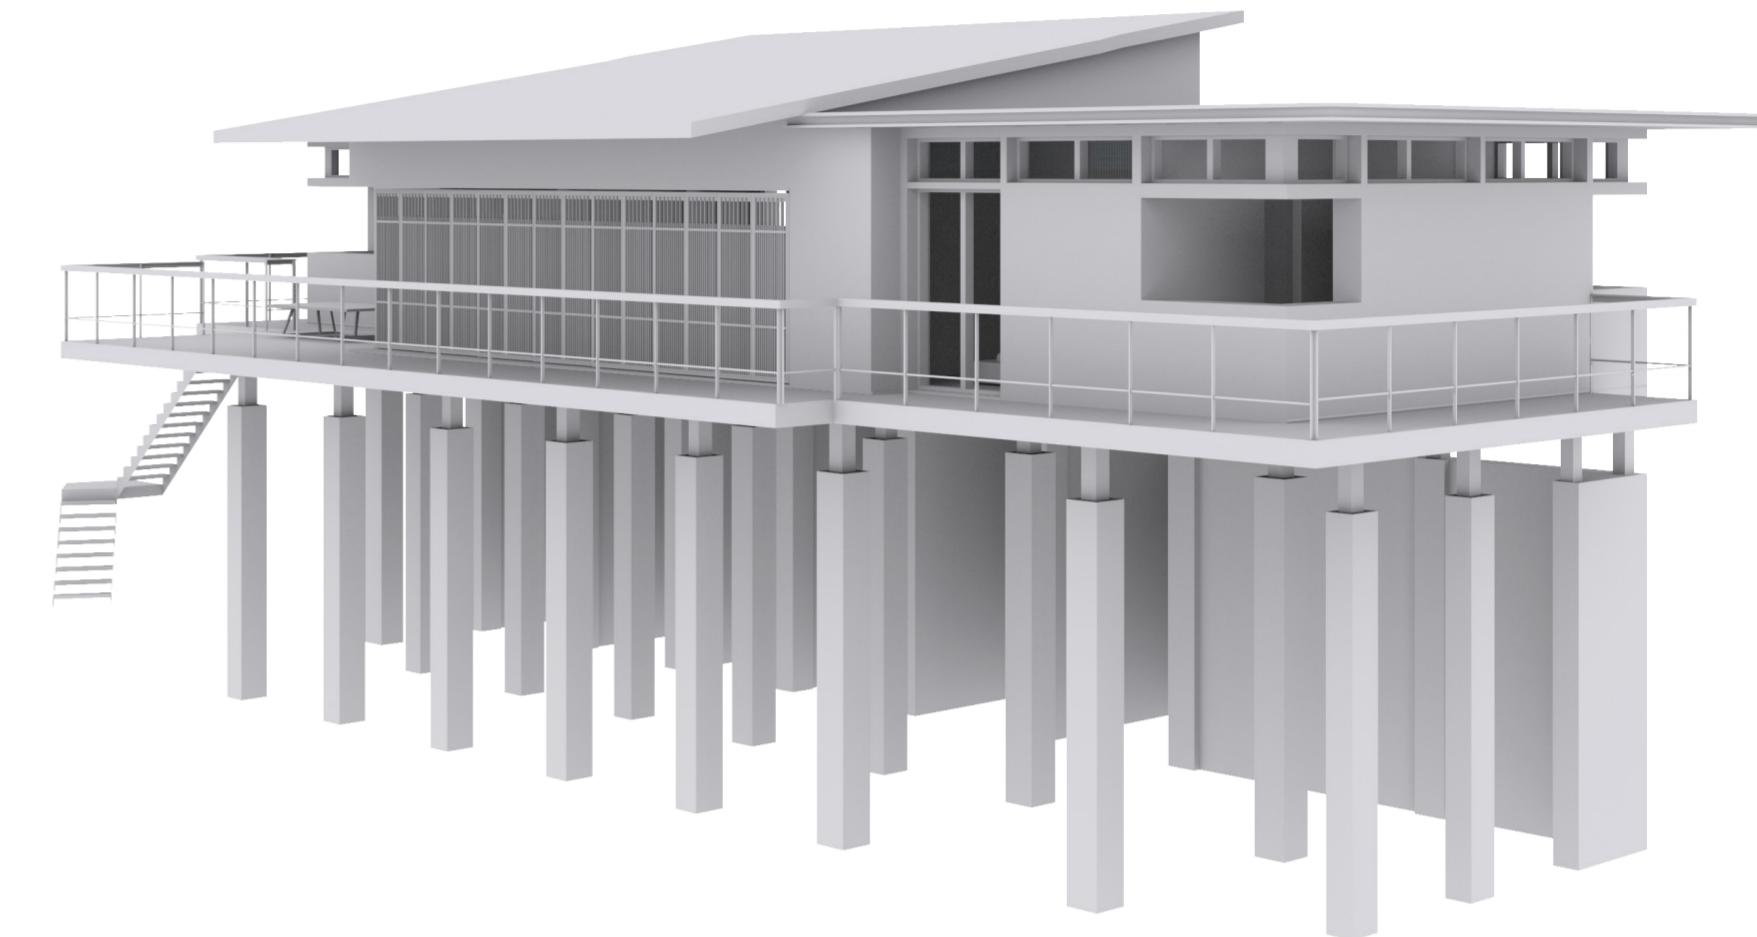


PROSPETTIVA

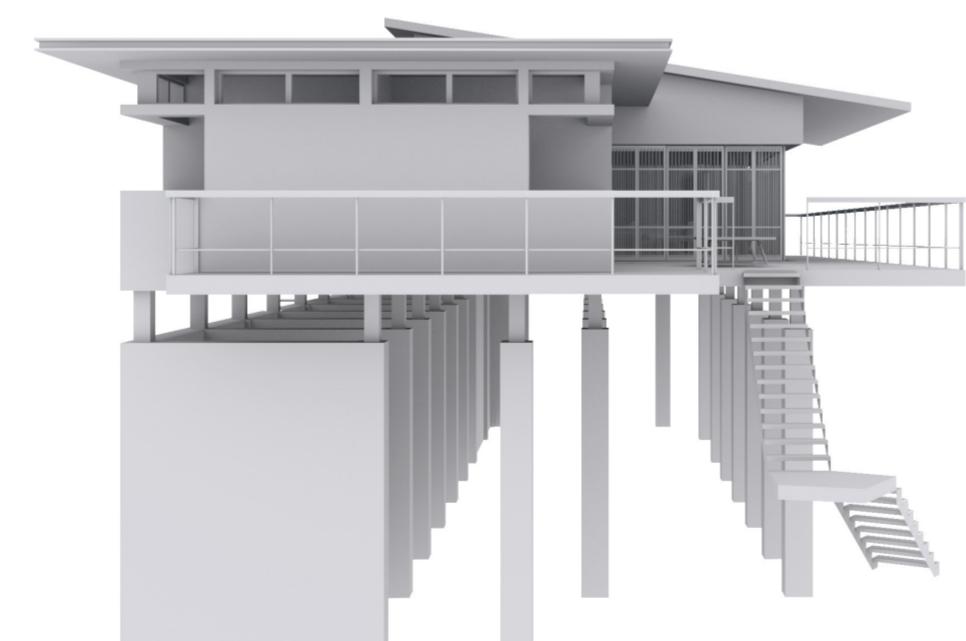



PROSPETTO NORD-EST

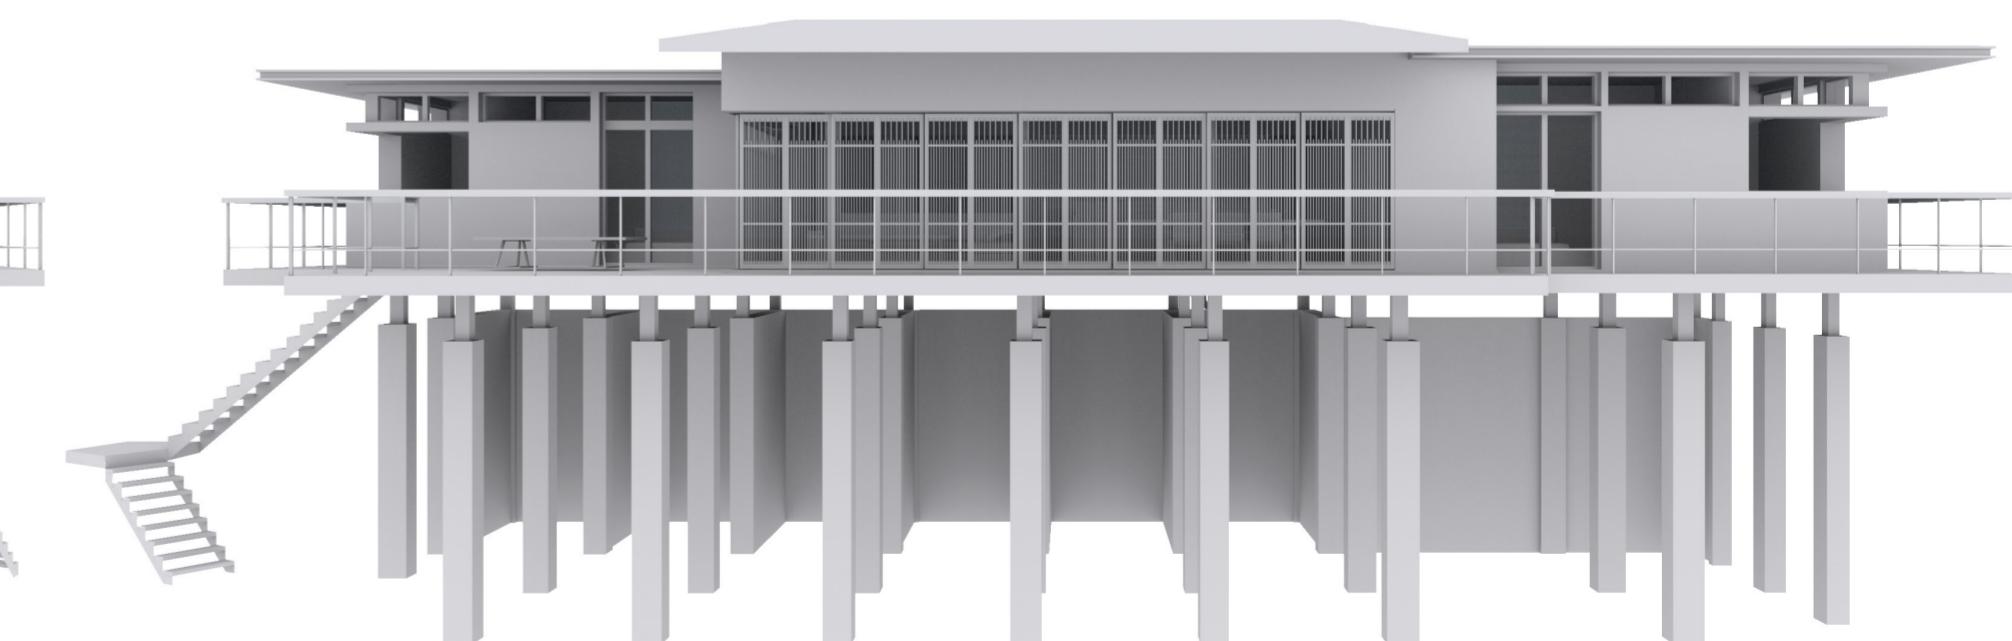


PROSPETTO NORD-OVEST

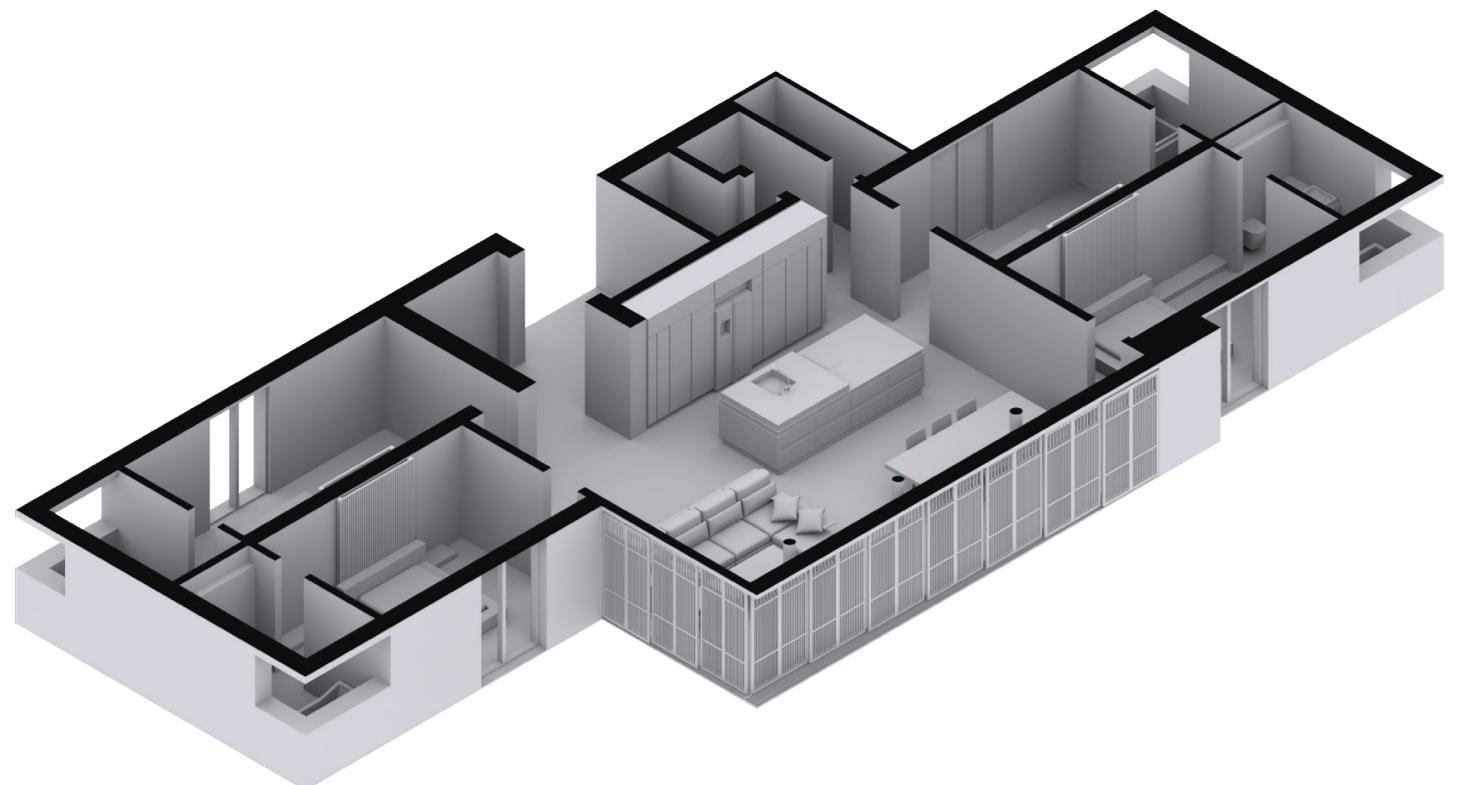

SPACCATO ASSONOMETRICO

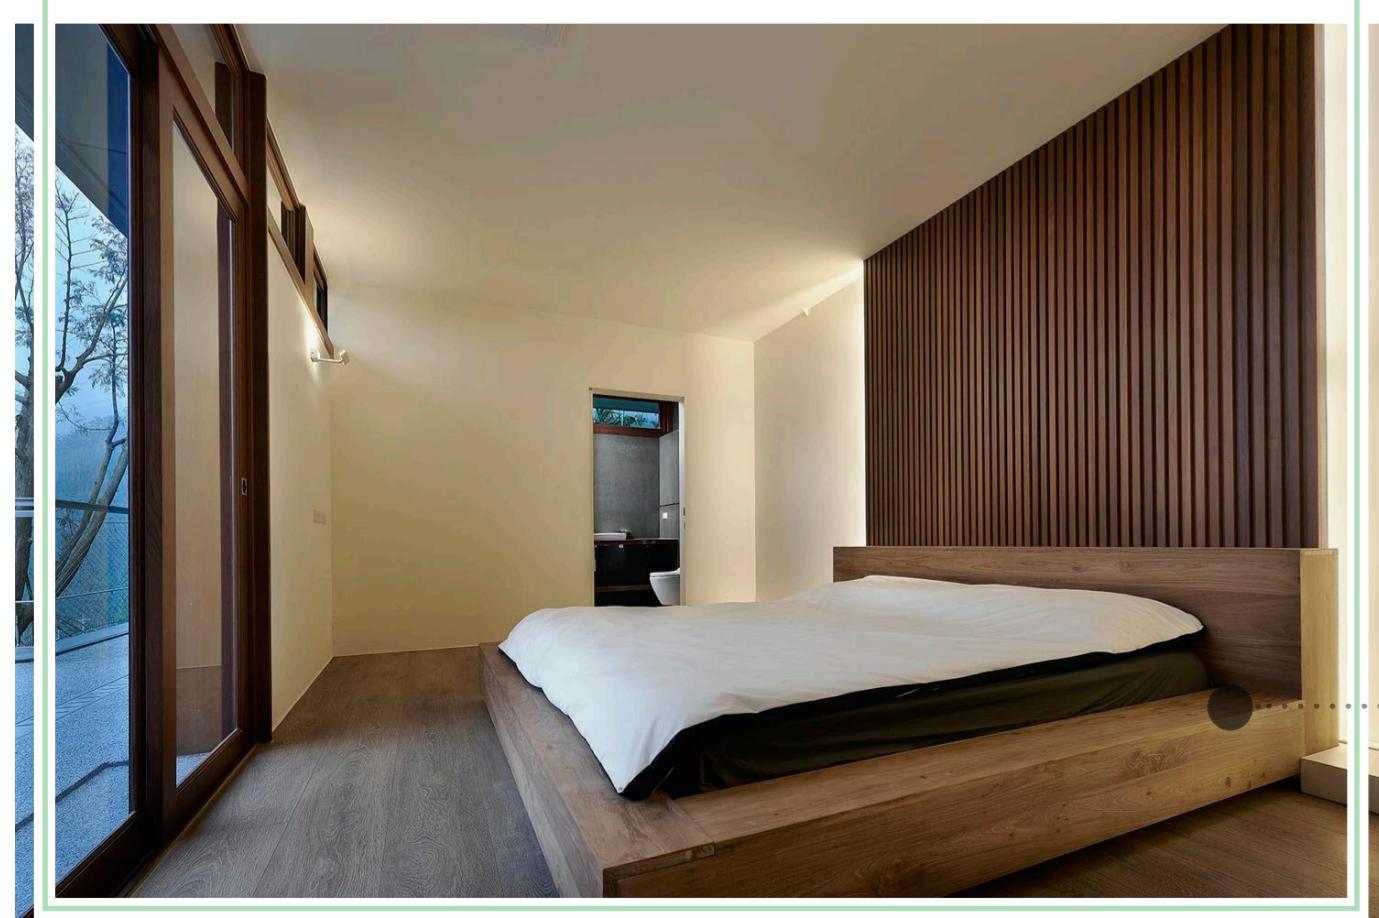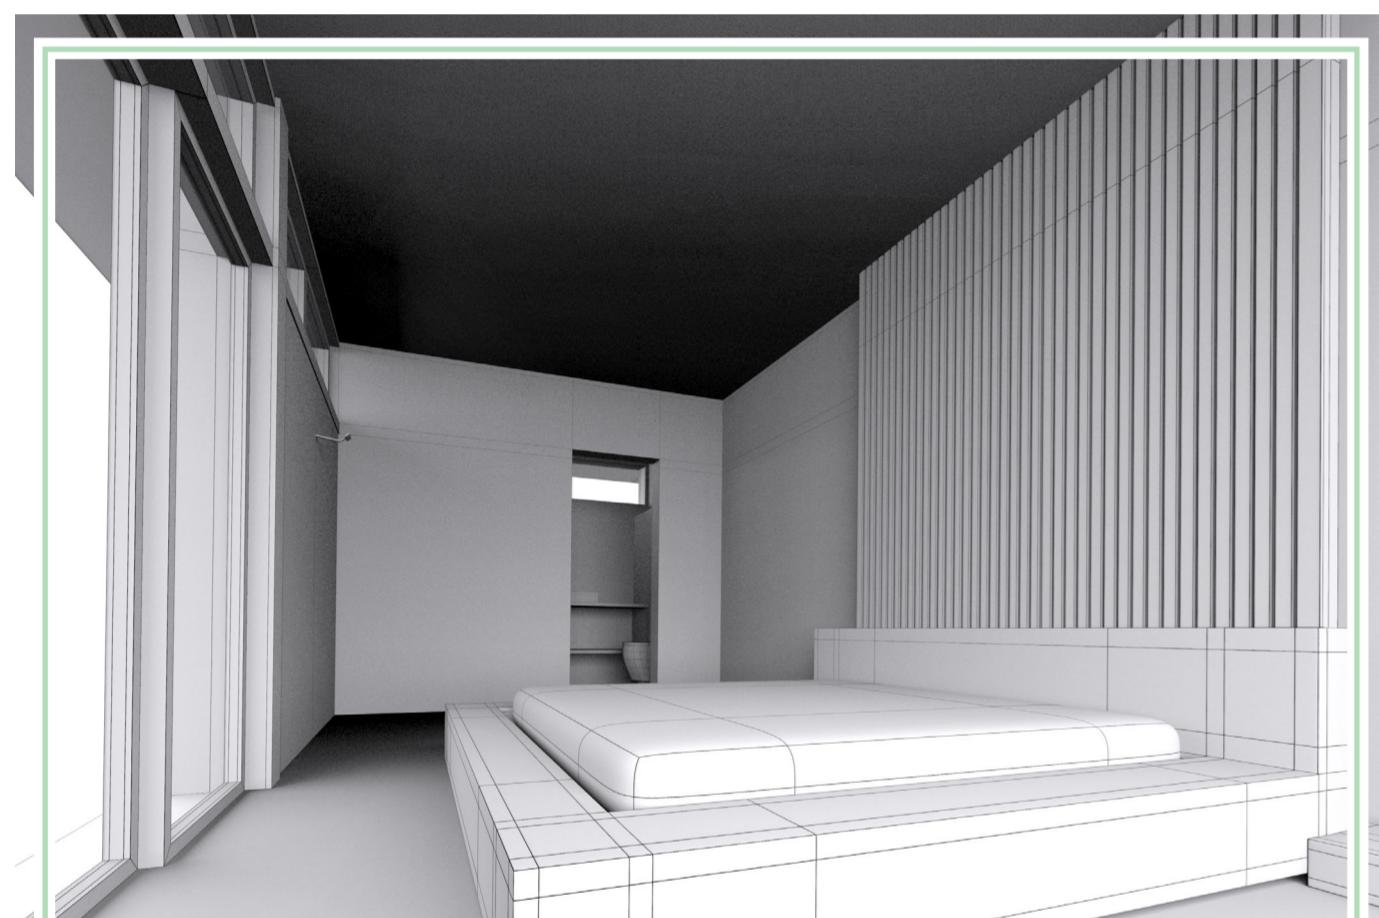

PIANTA

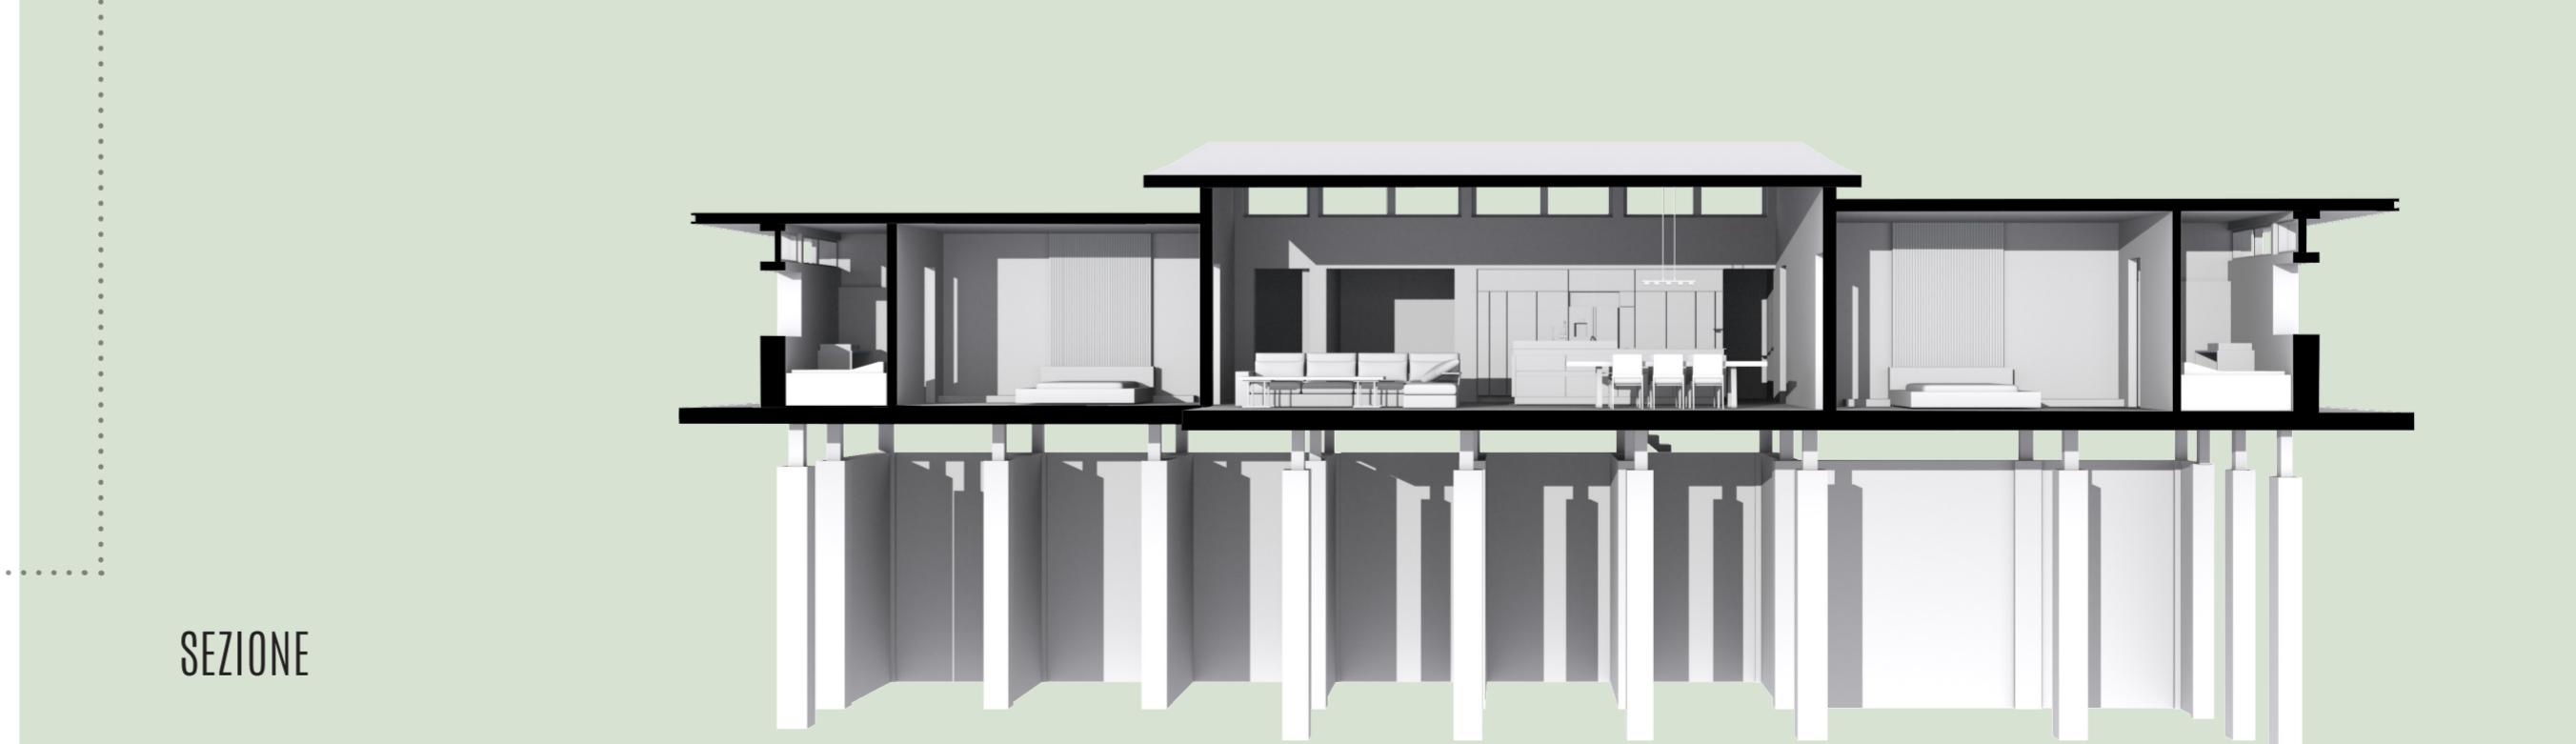

SEZIONE